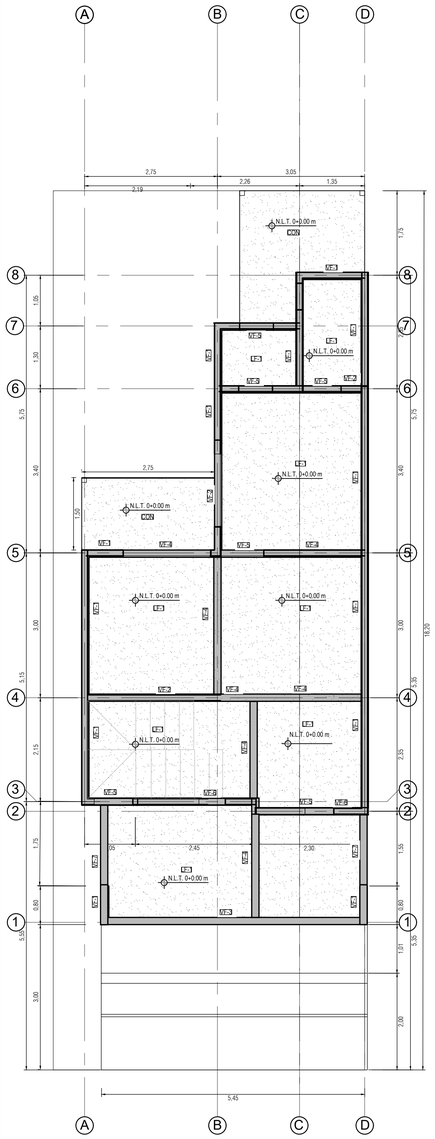

PLANTA ESTRUCTURAL DE FUNDACIONES NIVEL 0+0,00 m

ESCALA 1:50

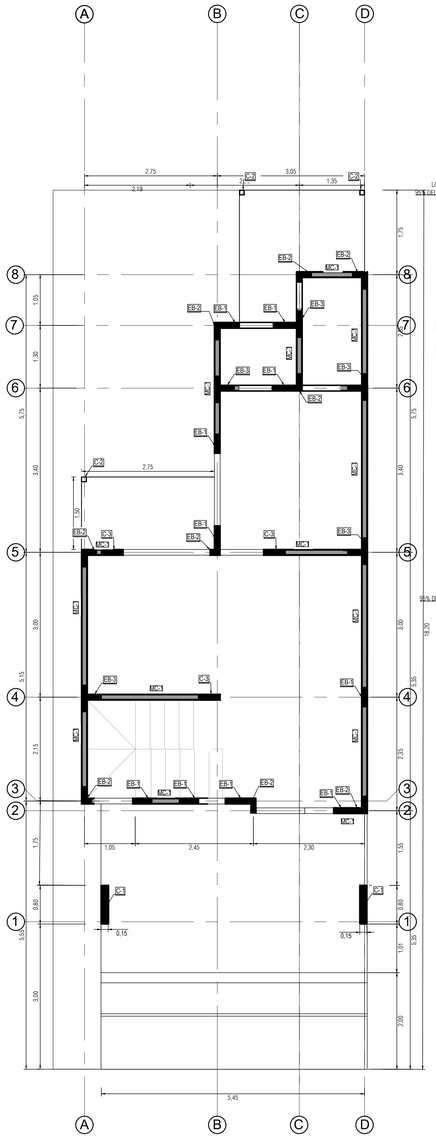

PLANTA ESTRUCTURAL DE MUROS Y COLUMNAS NIVEL 0+0,00 m

ESCALA 1:50

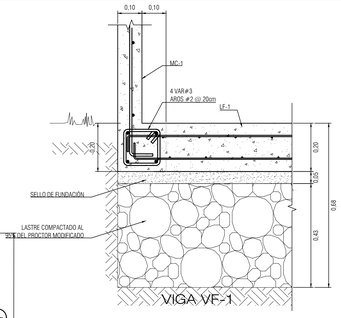

VIGA VF-1

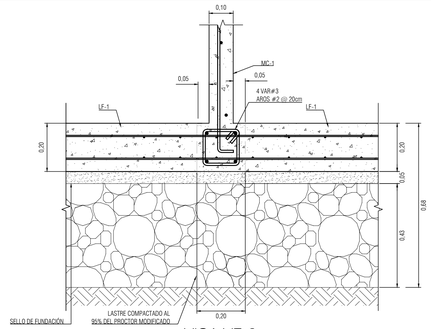

VIGA VF-2

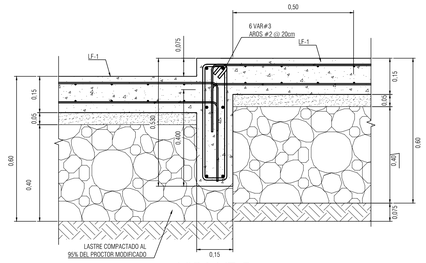

VIGA VF-5

DETALLE DE VIGAS DE FUNDACIÓN EXTERNA BAJO PARED

ESCALA 1:10

DETALLE DE VIGAS DE FUNDACIÓN INTERNA BAJO PARED

ESCALA 1:10

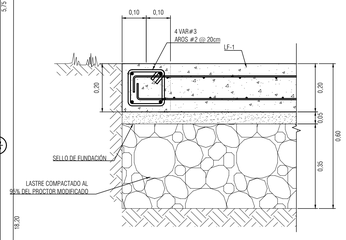

VIGA VF-3

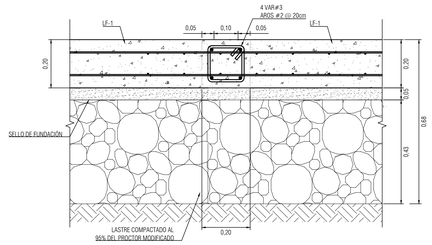

VIGA VF-4

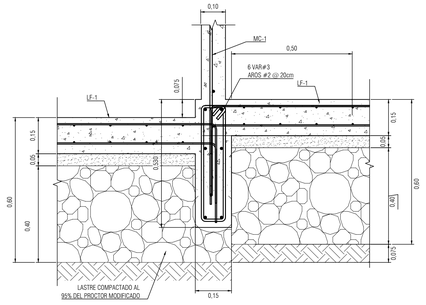

VIGA VF-6

DETALLE DE VIGAS DE FUNDACIÓN EXTERNA SIN PARED ARRIBA

ESCALA 1:10

DETALLE DE VIGAS DE FUNDACIÓN INTERNA SIN PARED ARRIBA

ESCALA 1:10

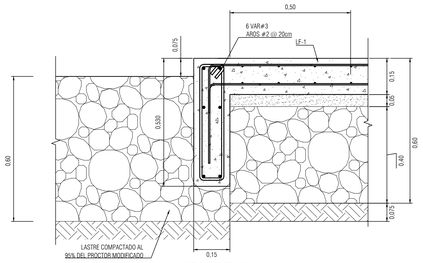

VIGA VF-7

DETALLE DE C-2

ESCALA 1:5

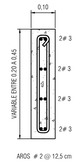

DETALLE DE C-3

ESCALA 1:10

DETALLE DE MURO DE CONCRETO MC-1

ESCALA 1:10

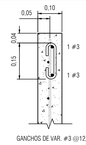

DETALLE DE VIGA BANQUINA VB-1

ESCALA 1:10

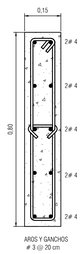

DETALLE DE C-1

ESCALA 1:10

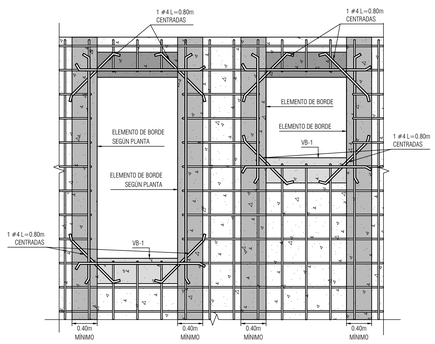

DETALLE DE REFUERZO DIAGONAL ADICIONAL EN BUQUES DE PUERTAS Y VENTANAS

ESCALA 1:15

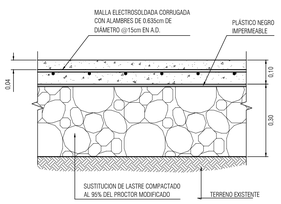

DETALLE DE CONTRAPISO CON-1

ESCALA 1:10

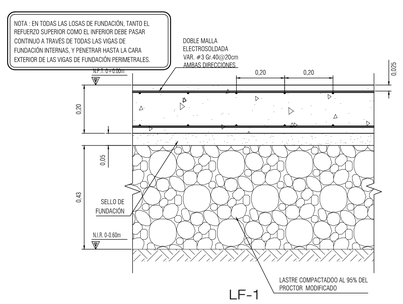

LF-1

DETALLES DE LOSAS DE FUNDACIÓN CASAS DE DOS NIVELES

ESCALA 1:10

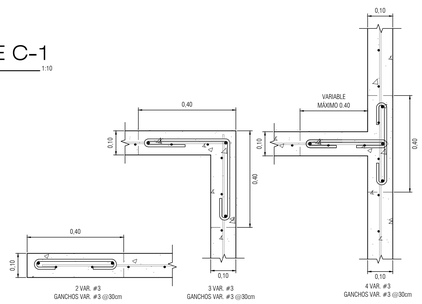

NOTAS:
- EL REFUERZO VERTICAL Y HORIZONTAL DEL MURO DEBE CONTINUAR EN TODA LA REGIÓN DEL ELEMENTO DE BORDE

DETALLE DE ELEMENTOS DE BORDE

ESCALA 1:10

NOMENCLATURA GENERAL

N.P.T.	NIVEL DE PISO TERMINADO
N.S.P.	NIVEL SUPERIOR DE PLACA
N.I.P.	NIVEL INFERIOR DE PLACA
N.S.VF.	NIVEL SUPERIOR DE VIGA DE FUNDACIÓN
N.I.VF.	NIVEL INFERIOR DE VIGA DE FUNDACIÓN
N.S.LF.	NIVEL SUPERIOR DE LOSA DE FUNDACIÓN
N.I.LF.	NIVEL INFERIOR DE LOSA DE FUNDACIÓN
N.S.VE.	NIVEL SUPERIOR DE VIGA DE ENTREPISO
N.I.VE.	NIVEL INFERIOR DE VIGA DE ENTREPISO
N.S.VC.	NIVEL SUPERIOR DE VIGA CORONA
N.I.VC.	NIVEL INFERIOR DE VIGA CORONA
N.S.VT.	NIVEL SUPERIOR DE VIGA DE TECHO
N.I.VT.	NIVEL INFERIOR DE VIGA DE TECHO
N.S.M.	NIVEL SUPERIOR DE MURO
N.I.M.	NIVEL INFERIOR DE MURO
N.S.L.	NIVEL SUPERIOR DE LOSA
N.I.L.	NIVEL INFERIOR DE LOSA
VTA-	VIGA TAPICHEL
VC-	VIGA CORONA
VT-	VIGA DE TECHO
VX-	VIGA CARGADOR
VB-	VIGA BANQUINA
CL-	CLAVADOR
VES-	VIGA DE ESCALERA
CES-	COLUMNA ESCALERA
E-	ENTREPISO
ES-	ESCALERA
L-	LOSA DE TECHO
AP-	DETALLE DE APOYO
APT-	DETALLE DE APOYO DE TECHO
PA-	PLACA AISLADA DE FUNDACIÓN
LF-	LOSA DE FUNDACIÓN
VF-	VIGA DE FUNDACIÓN
C-	COLUMNA
PE-	PEDESTALES
MM-	MURO DE MAMPOSTERÍA
MC-	MURO DE CONCRETO
MO-	MOCHETA
VE-	VIGA DE ENTREPISO

SIMBOLOGIA GENERAL

N.P.T. 0+0.00 m	INDICACIÓN DE NIVELES EN ELEVACIÓN
N.P.T. 0+0.00 m	INDICACION DE NIVELES EN PLANTA
	INDICACION DE TERRENO
A	INDICACIÓN DE EJE
	INDICACIÓN DE VIGUETAS EN ENTREPISO
A	INDICACIÓN DE SECCIÓN
	INDICACIÓN DE APOYO
S=0% RAMPA %	INDICACIÓN EN ESCALERAS O RAMPAS
	PLACAS DE FUNDACIÓN
	VIGAS DE AMARRE
	VIGAS BANQUINA
	MUROS
	PARED LIVIANA
	COLUMNA O MOCHETA
	VIGAS DE ENTREPISO, CORONA, TECHO O TAPICHEL
	ANGULAR DE APOYO DE CLAVADOR
	CLAVADOR DE TECHO
	RELLENO DE LASTRE
	INDICACIÓN DE TERRENO

CONTENIDO:

- PLANTA ESTRUCTURAL DE FUNDACIONES
- DETALLES DE VIGAS DE FUNDACIÓN
- DETALLE DE CONTRAPISO
- PLANTA DE COLUMNAS Y MUROS PRIMER NIVEL
-DETALLES DE COLUMNAS Y ELEMENTOS DE BORDE

INFORMACIÓN REGISTRO PÚBLICO

PROPIETARIO: ADELANTE DESARROLLOS S.A.
Nº CATASTRO: C-56154-2025
SITAS: 3 00246942F-000

FECHA	LÁMINA
FEBRERO 2026	S02/ S05