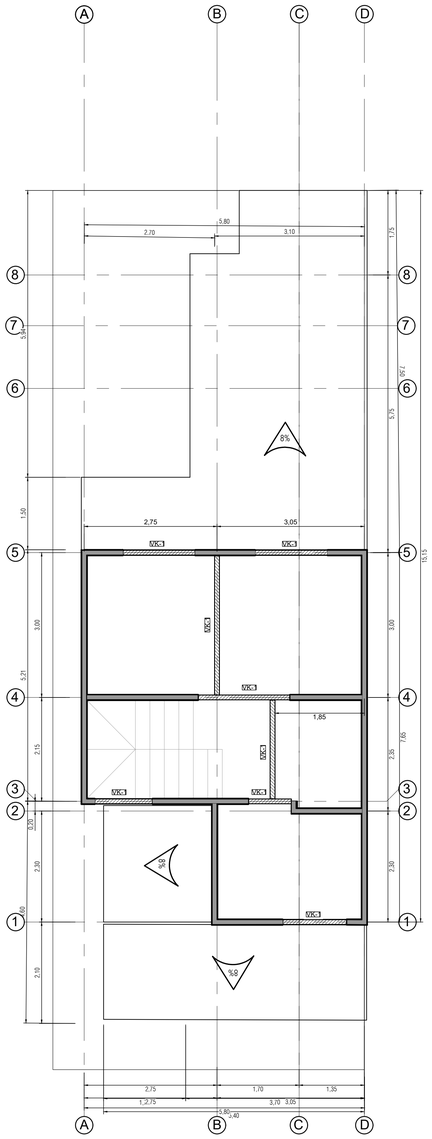

PLANTA ESTRUCTURAL
DE VIGAS CORONA

NIVEL 0+5.50 m

ESCALA 1:50

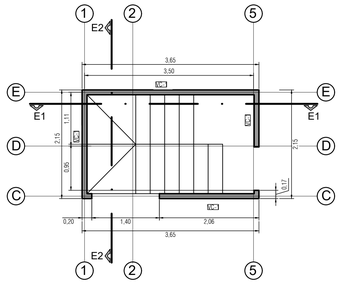

PLANTA DE VIGAS DE ESCALERA

ESCALA 1:50

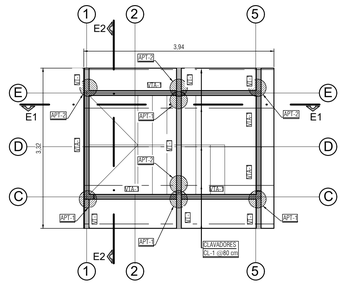

PLANTA DE TECHO DE ESCALERA

ESCALA 1:50

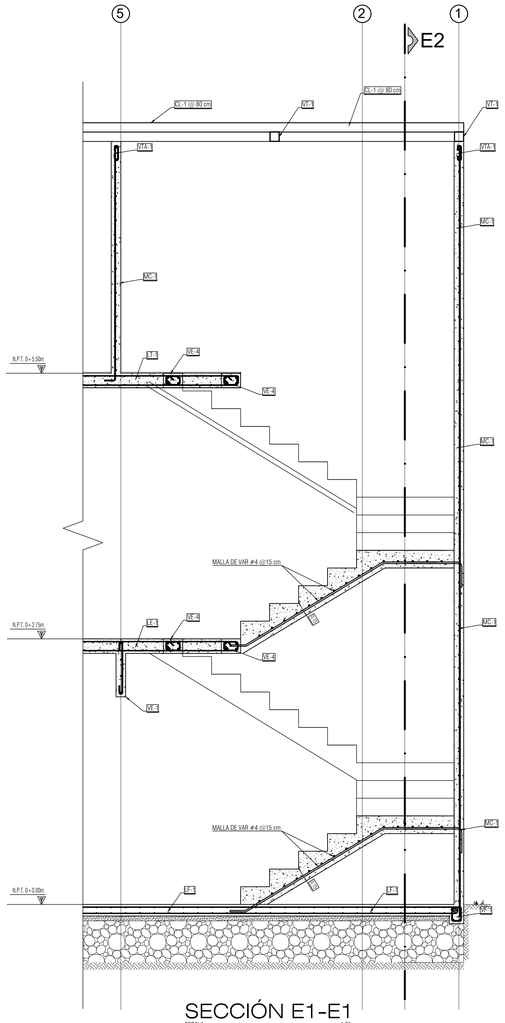

SECCIÓN E1-E1

ESCALA 1:25

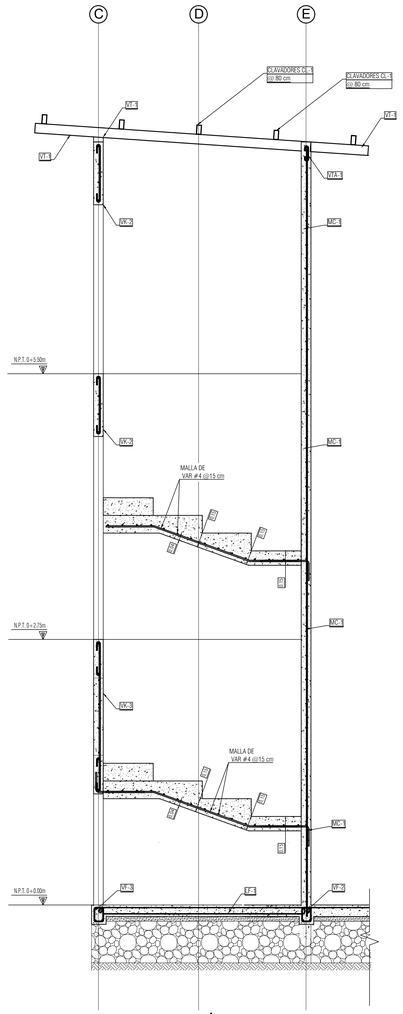

SECCIÓN E2-E2

ESCALA 1:25

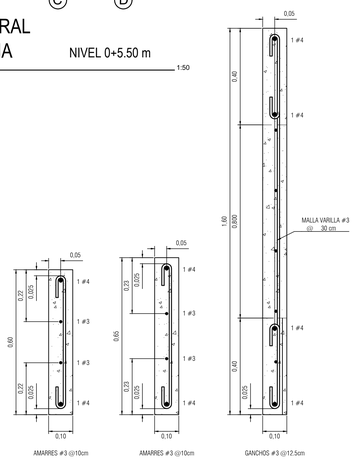

AMARRES #3 @10cm — VK-1

AMARRES #3 @10cm — VK-2

GANCHOS #3 @12.5cm — VK-3

DETALLES DE
VIGAS CARGADOR

ESCALA 1:10

NOMENCLATURA GENE

N.P.T.	NIVEL DE PISO TERMINADO
N.S.P.	NIVEL SUPERIOR DE PLACA
N.I.P.	NIVEL INFERIOR DE PLACA
N.S.VF.	NIVEL SUPERIOR DE VIGA DE FU
N.I.VF.	NIVEL INFERIOR DE VIGA DE FUN
N.S.LF.	NIVEL SUPERIOR DE LOSA DE FU
N.I.LF.	NIVEL INFERIOR DE LOSA DE FUN
N.S.VE.	NIVEL SUPERIOR DE VIGA DE EN
N.I.VE.	NIVEL INFERIOR DE VIGA DE ENT
N.S.VC.	NIVEL SUPERIOR DE VIGA CORO
N.I.VC.	NIVEL INFERIOR DE VIGA CORON
N.S.VT.	NIVEL SUPERIOR DE VIGA DE TE
N.I.VT.	NIVEL INFERIOR DE VIGA DE TEC
N.S.M.	NIVEL SUPERIOR DE MURO
N.I.M.	NIVEL INFERIOR DE MURO
N.S.L.	NIVEL SUPERIOR DE LOSA
N.I.L.	NIVEL INFERIOR DE LOSA
VTA-	VIGA TAPICHEL
VC-	VIGA CORONA
VT-	VIGA DE TECHO
VC-	VIGA CARGADOR
VB-	VIGA BANQUINA
CL-	CLAVADOR
VES-	VIGA DE ESCALERA
CES-	COLUMNA ESCALERA
E-	ENTREPISO
ES-	ESCALERA
LT-	LOSA DE TECHO
AP-	DETALLE DE APOYO
APT-	DETALLE DE APOYO DE TECHO
PA-	PLACA AISLADA DE FUNDACIÓN
LF-	LOSA DE FUNDACIÓN
VF-	VIGA DE FUNDACIÓN
C-	COLUMNA
PE-	PEDESTALES
MM-	MURO DE MAMPOSTERÍA
MC-	MURO DE CONCRETO
EB-	EBCHETA
VE-	VIGA DE ENTREPISO

SIMBOLOGIA GENERAL

INDICACIÓN DE NIVELES EN ELEVACIÓN	PLACAS DE FUNDACIÓN
INDICACIÓN DE NIVELES EN PLANTA	VIGAS DE AMARRE
INDICACIÓN DE TERRENO	VIGAS BANQUINA
INDICACIÓN DE EJE	MUROS
INDICACIÓN DE VIGUETAS EN ENTREPISO	PARED LIVIANA
INDICACIÓN DE SECCIÓN	COLUMNA O EBCHETA
INDICACIÓN DE APOYO	VIGAS DE ENTREPISO, CORONA, TECHO O TAPICHEL
INDICACIÓN EN ESCALERAS O RAMPAS	ANGULAR DE APOYO DE CLAVADOR
	CLAVADOR DE TECHO
	RELLENO DE LASTRE
	INDICACIÓN DE TERRENO

CONTENIDO:

- PLANTA ESTRUCTURAL DE MUROS Y COLUMNAS
- PLANTA ESTRUCTURAL DE VIGAS CORONA
- DETALLE DE EBCHETAS, COLUMNAS
- DETALLE DE VIGAS CORONA Y CARGADOR

INFORMACIÓN REGISTRO PÚBLICO

PROPIETARIO: ADELANTE DESARROLLOS S.A.

Nº CATASTRO: C-56154-2025

SITAS: 3 00246942F-000

FECHA	LÁMINA
FEBRERO 2026	S04/ S05