NOTAS INSTALACIONES MECÁNICAS

GENERAL:

Todas las instalaciones mecánicas se realizarán en apego al código de instalaciones hidráulicas en Edificaciones de el Colegio Federado de Ingenieros y Arquitectos de Costa Rica y Reglamentación técnica para Diseño y construcción de urbanizaciones, condominios y fraccionamientos del instituto Costarricense de Acueductos y Alcantarillados. Así como demás instituciones gubernamentales nacionales que regulan la materia, los planos mecánicos son esquemáticos por lo tanto el contratista esta obligado a coordinar con las demás disciplinas involucradas cada elemento a instalar.
El contratista deberá verificar en sitio los niveles y pasos de tuberías a través de muros, vigas y cimentaciones, así como coordinar para dejar los respectivos pasantes de tuberías.
Todos los elementos y accesorios de los diferentes sistemas deberán instalarse en estricto apego a las recomendaciones del fabricante y las buenas prácticas constructivas, el contratista será responsable por la instalación correcta, aunque no se muestre en detalle la instalación de los diferentes elementos.

AGUA POTABLE:

El sistema de suministro de agua potable indicado en planos es esquemático, todas las previstas deberán ser ubicadas de acuerdo con los muebles y piezas sanitarias en coordinación con planos arquitectónicos y estructurales. Todas las tuberías enterradas serán en PVC-SCH 40 para tuberías menos de 13 mm de diámetro y en PVC-SDR-17 para tuberías mayores, todas estas tuberías deberán ser nuevas, segmentadas, limpiadas y aprobadas antes de entrar en funcionamiento.
La tubería expuesta será en cobre tipo "M" para residencias, salvo que se indique lo contrario, esta deberá ser soldada con aleación de plomo y estaño, soportadas y pintada de color verde y llevara la etiqueta que diga "SAP" y con una flecha indicando el sentido de flujo.

AGUA CALIENTE:

El sistema de suministro de agua caliente será en tubería de CPVC para tuberías enterradas y empotradas en paredes deberá ir aislada con fibra de vidrio de 25mm de espesor como mínimo y encamisada con chaqueta de PVC. Las tuberías expuestas serán en cobre tipo "L" con aislamiento de fibra de vidrio de 25mm de espesor como mínimo y encamisada con chaqueta de PVC, esta tubería deberá contar con juntas de expansión a lo largo de la tubería, deberá ser soportada y pintada de color rojo con rayas blancas transversales y con etiqueta que indique "SAC".

AGUAS NEGRAS Y JABONOSAS:

El sistema de drenaje de aguas negras y jabonosas se realizará en tubería de PVC-SDR-32.5 cuando este viaje por zonas verdes o bajo contrapisos, cuando esta se coloque en zonas de transito pesado o expuesta bajo entrepisos deberá ser en PVC-SDR-26. Las pendientes mínimas para tuberías de drenaje serán de 1.5% para tuberías mayores o iguales a 75mm de diámetro y 2% para tuberías menores de 75mm de diámetro. En todos los cambios de dirección deberá proveerse de un registro de piso, las conexiones a las piezas sanitarias deberán hacerse mediante un sifón con registro o trampa tipo "P" no se permitirá el uso de "Tees" sanitarias en tramos horizontales, solo en tramos de tuberías verticales. Todos los cambios de dirección serán con codos a 45° y con "Yee" y tapón roscado antes de que la tubería sea embebida en el piso. Las tuberías expuestas deberán llevar etiquetas que indique "DAJ" o en el caso de tuberías de aguas negras la etiqueta deberá indicar "DAN", y con una flecha indicando el sentido de flujo. Cuando la tubería de drenaje de aguas jabonosas deba conectarse a la red de aguas negras se deberá instalar antes de la conexión un registro sifónico.

VENTILACIÓN SANITARÍA:

Todo aparato sanitario y drenaje de piso deberá llevar una tubería de ventilación inmediatamente después del sifón de diámetro adecuado y con pendiente de 1% hacia la pieza sanitaria. El diámetro mínimo de tubería de ventilación a utilizar será de 38mm, la tubería a utilizar será en PVC-SDR32.5. Se deberán respetar las distancias mínimas establecidas en el Código de instalaciones sanitarias de edificaciones del Colegio Federado de Ingenieros y Arquitectos de

SIMBOLOGIA DE DUCTOS	
SAP	SUBE AGUA POTABLE
VAG	VIENEN AGUAS GRISES
VAN	VIENEN AGUAS NEGRAS
SAP	SUBE AGUA POTABLE
BAG	BAJAN AGUAS GRISES
BAN	BAJAN AGUAS NEGRAS

SIMBOLOGIA

- PVC 100mm Ø 2% Pend. Aguas Negras
- PVC 75mm Ø 2% Pend. Aguas Servidas
- PVC 100mm Ø 2% Pend. Aguas Pluviales
- PVC 13mm Ø Agua Potable Fria
- CPVC 13mm Ø Agua Potable Caliente
- C — Cenicero
- Conexión a Grifería
- Tee, Codo a 90°
- Yee
- RP — Drenaje de piso, con rejilla cromada o removible
- CR — Caja de Registro
- TG — Trampa de Grasa
- Sifón
- Acometida principal y Llave de paso

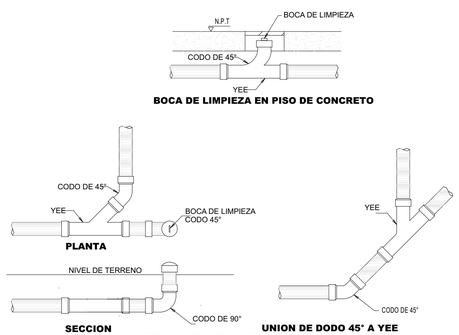

BOCA DE LIMPIEZA EN PISO DE CONCRETO

PLANTA

SECCION

UNION DE DODO 45° A YEE

DETALLE DE UNIONES
ESCALA 1 :15

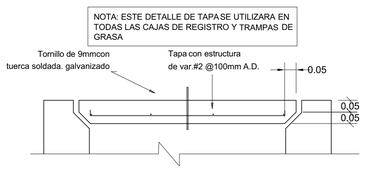

DET TAPA PARA CAJAS
SIN ESCALA

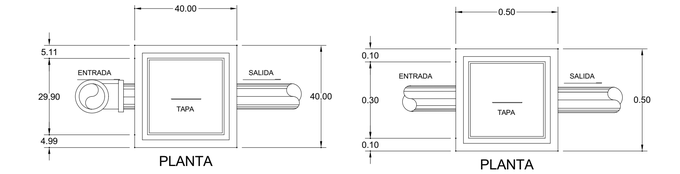

PLANTA

PLANTA

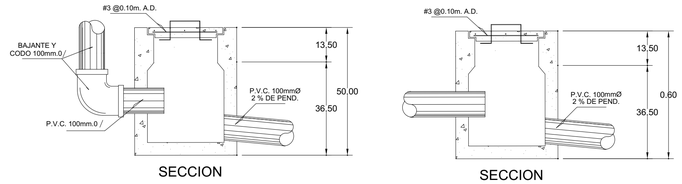

SECCION

SECCION

REGISTRO PARA AGUAS PLUVIALES
ESCALA 1 : 10

REGISTRO PARA AGUAS PLUVIALES
ESCALA 1 : 10

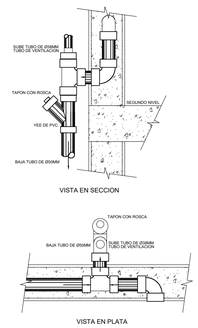

DIAGRAMA DE VENTILACION DE TUBERIAS DE AGUAS JABONOSAS

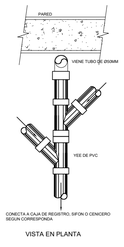

DIAGRAMA DE UNION DE TUBERIAS DE AGUAS JABONOSAS

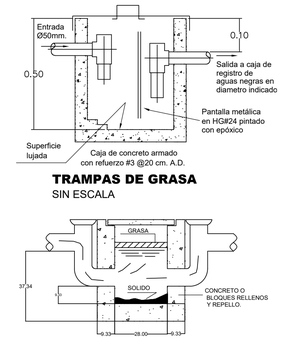

TRAMPAS DE GRASA
SIN ESCALA

DETALLE DE CENICERO
SIN ESCALA

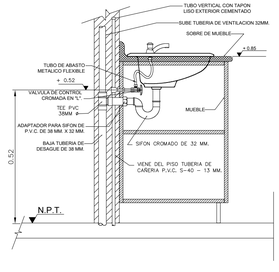

DETALLE DE INSTALACION DE LAVAMANOS
ESCALA 1:10

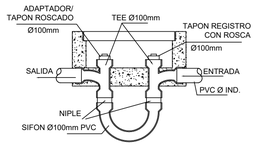

DETALLE DE SIFON
SIN ESCALA

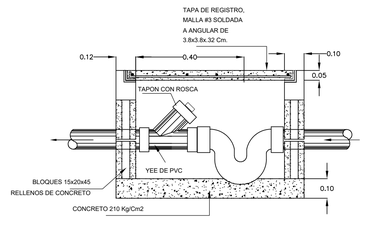

CAJA DE REGISTRO
SIN ESCALA

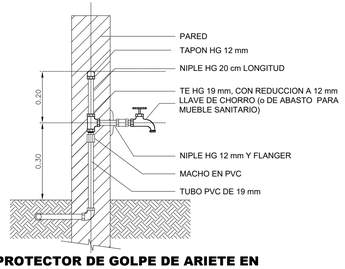

PROTECTOR DE GOLPE DE ARIETE EN SALIDA DE AGUA

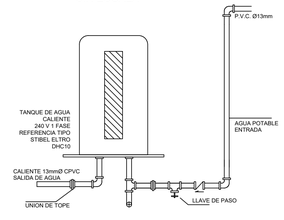

DET. DE TANQUE DE AGUA CALIENTE
SIN ESCALA

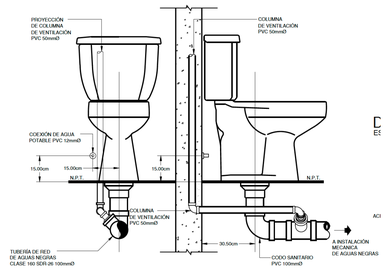

ZANTE 4D

INFORMACION REGISTRO PUBLICO:
Propietario: ADELANTE DESARROLLOS S.A / CÉDULA JURÍDICA 3-101-621790
No. Catastro: C-56154-2025
Folio Real: 3 00246942F-000

CONTENIDO:

INDICADO

ESCALA	FECHA	LAMINA
INDICADA	FEBRERO 2026	M-000